



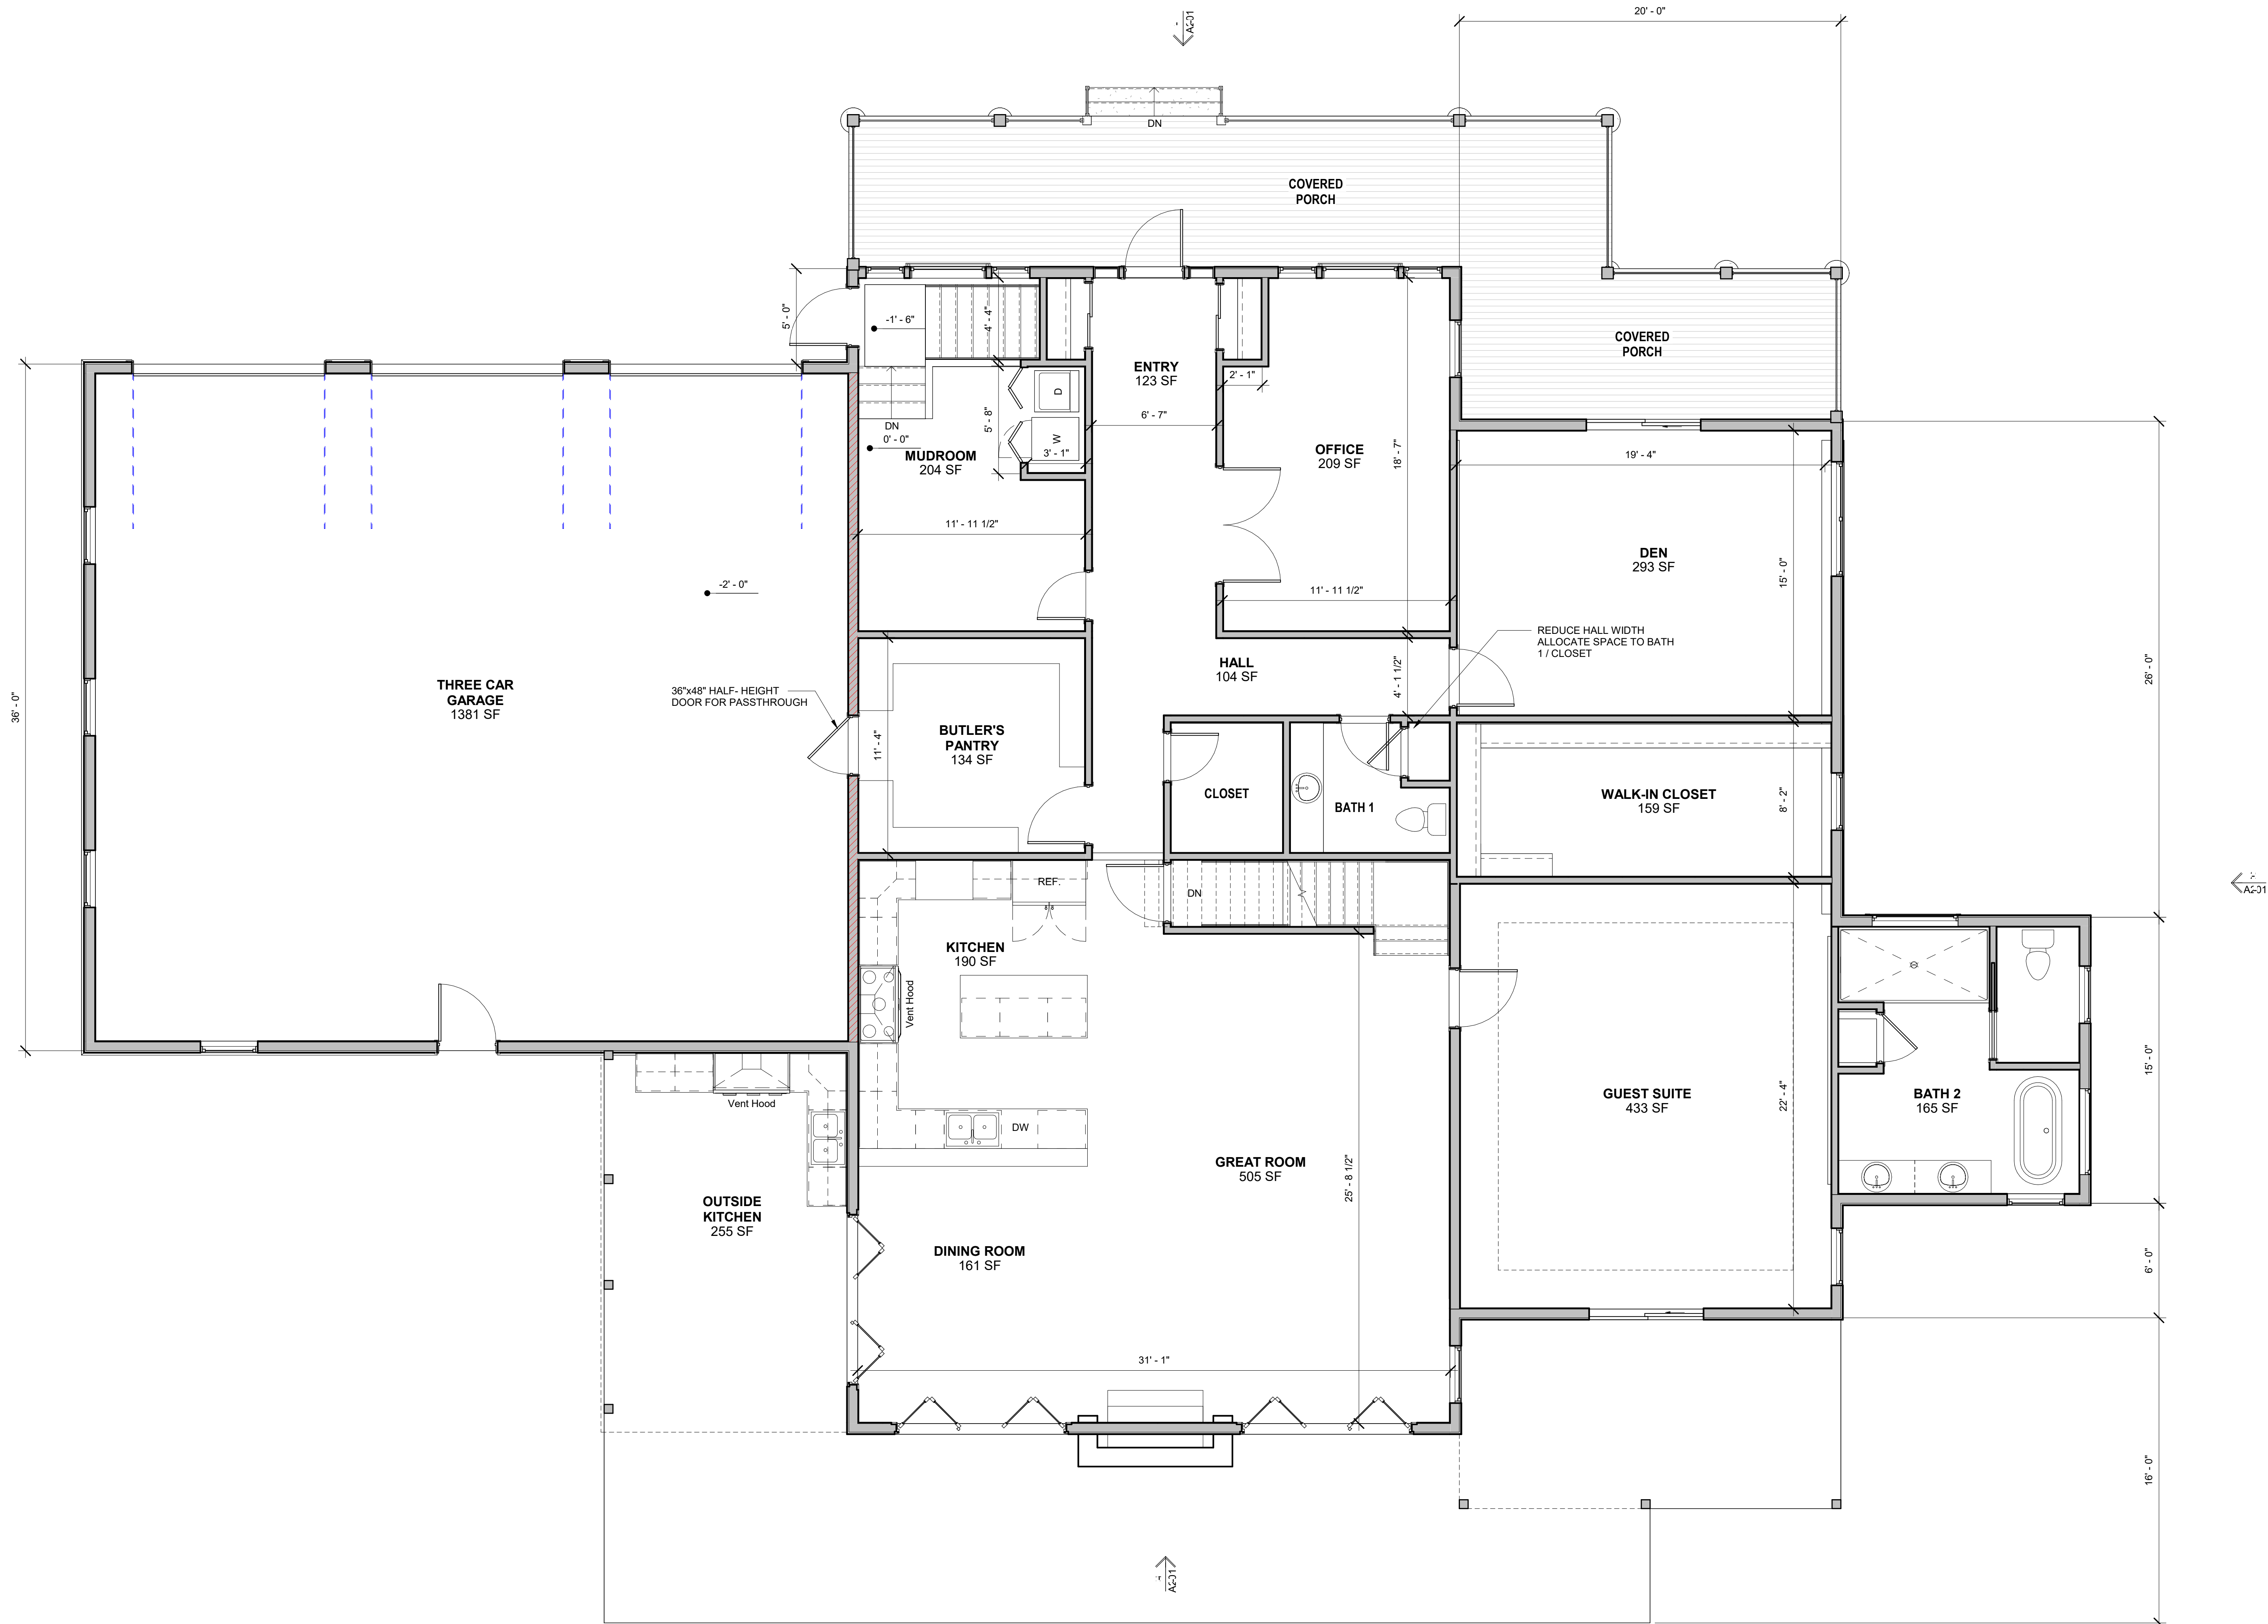

1 PROPOSED FLOOR PLAN
Ref: A201 / Scale: 1/4" = 1'-0"

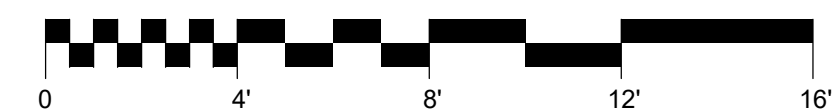

Project Location:

117 RED FOX RUN,
VESTAL, NY 13850

Project Name:

NEW RESIDENCE - ANELLO

Drawing Name:

PROPOSED FIRST
FLOOR PLAN

Designed by:

GRIFFITHS ENGINEERING

Drawn by:

DS

Checked by:

DG

Date:

07.31.2026

Project No.:


2026-106

Plot scale:

AS NOTED

Unauthorized alteration of
this drawing is a violation of
Professional Law, Section 2209,
subsection 2.


Seal

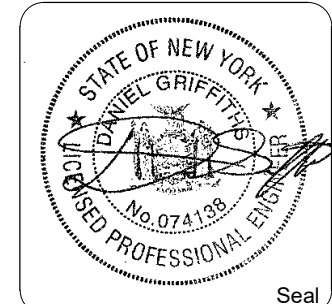

GRIFFITHS ENGINEERING
AND ARCHITECTURE, PLLC


33 Washington Street, Suite 2
Binghamton, New York 13903
T: (607) 724-2400
F: (607) 724-2436



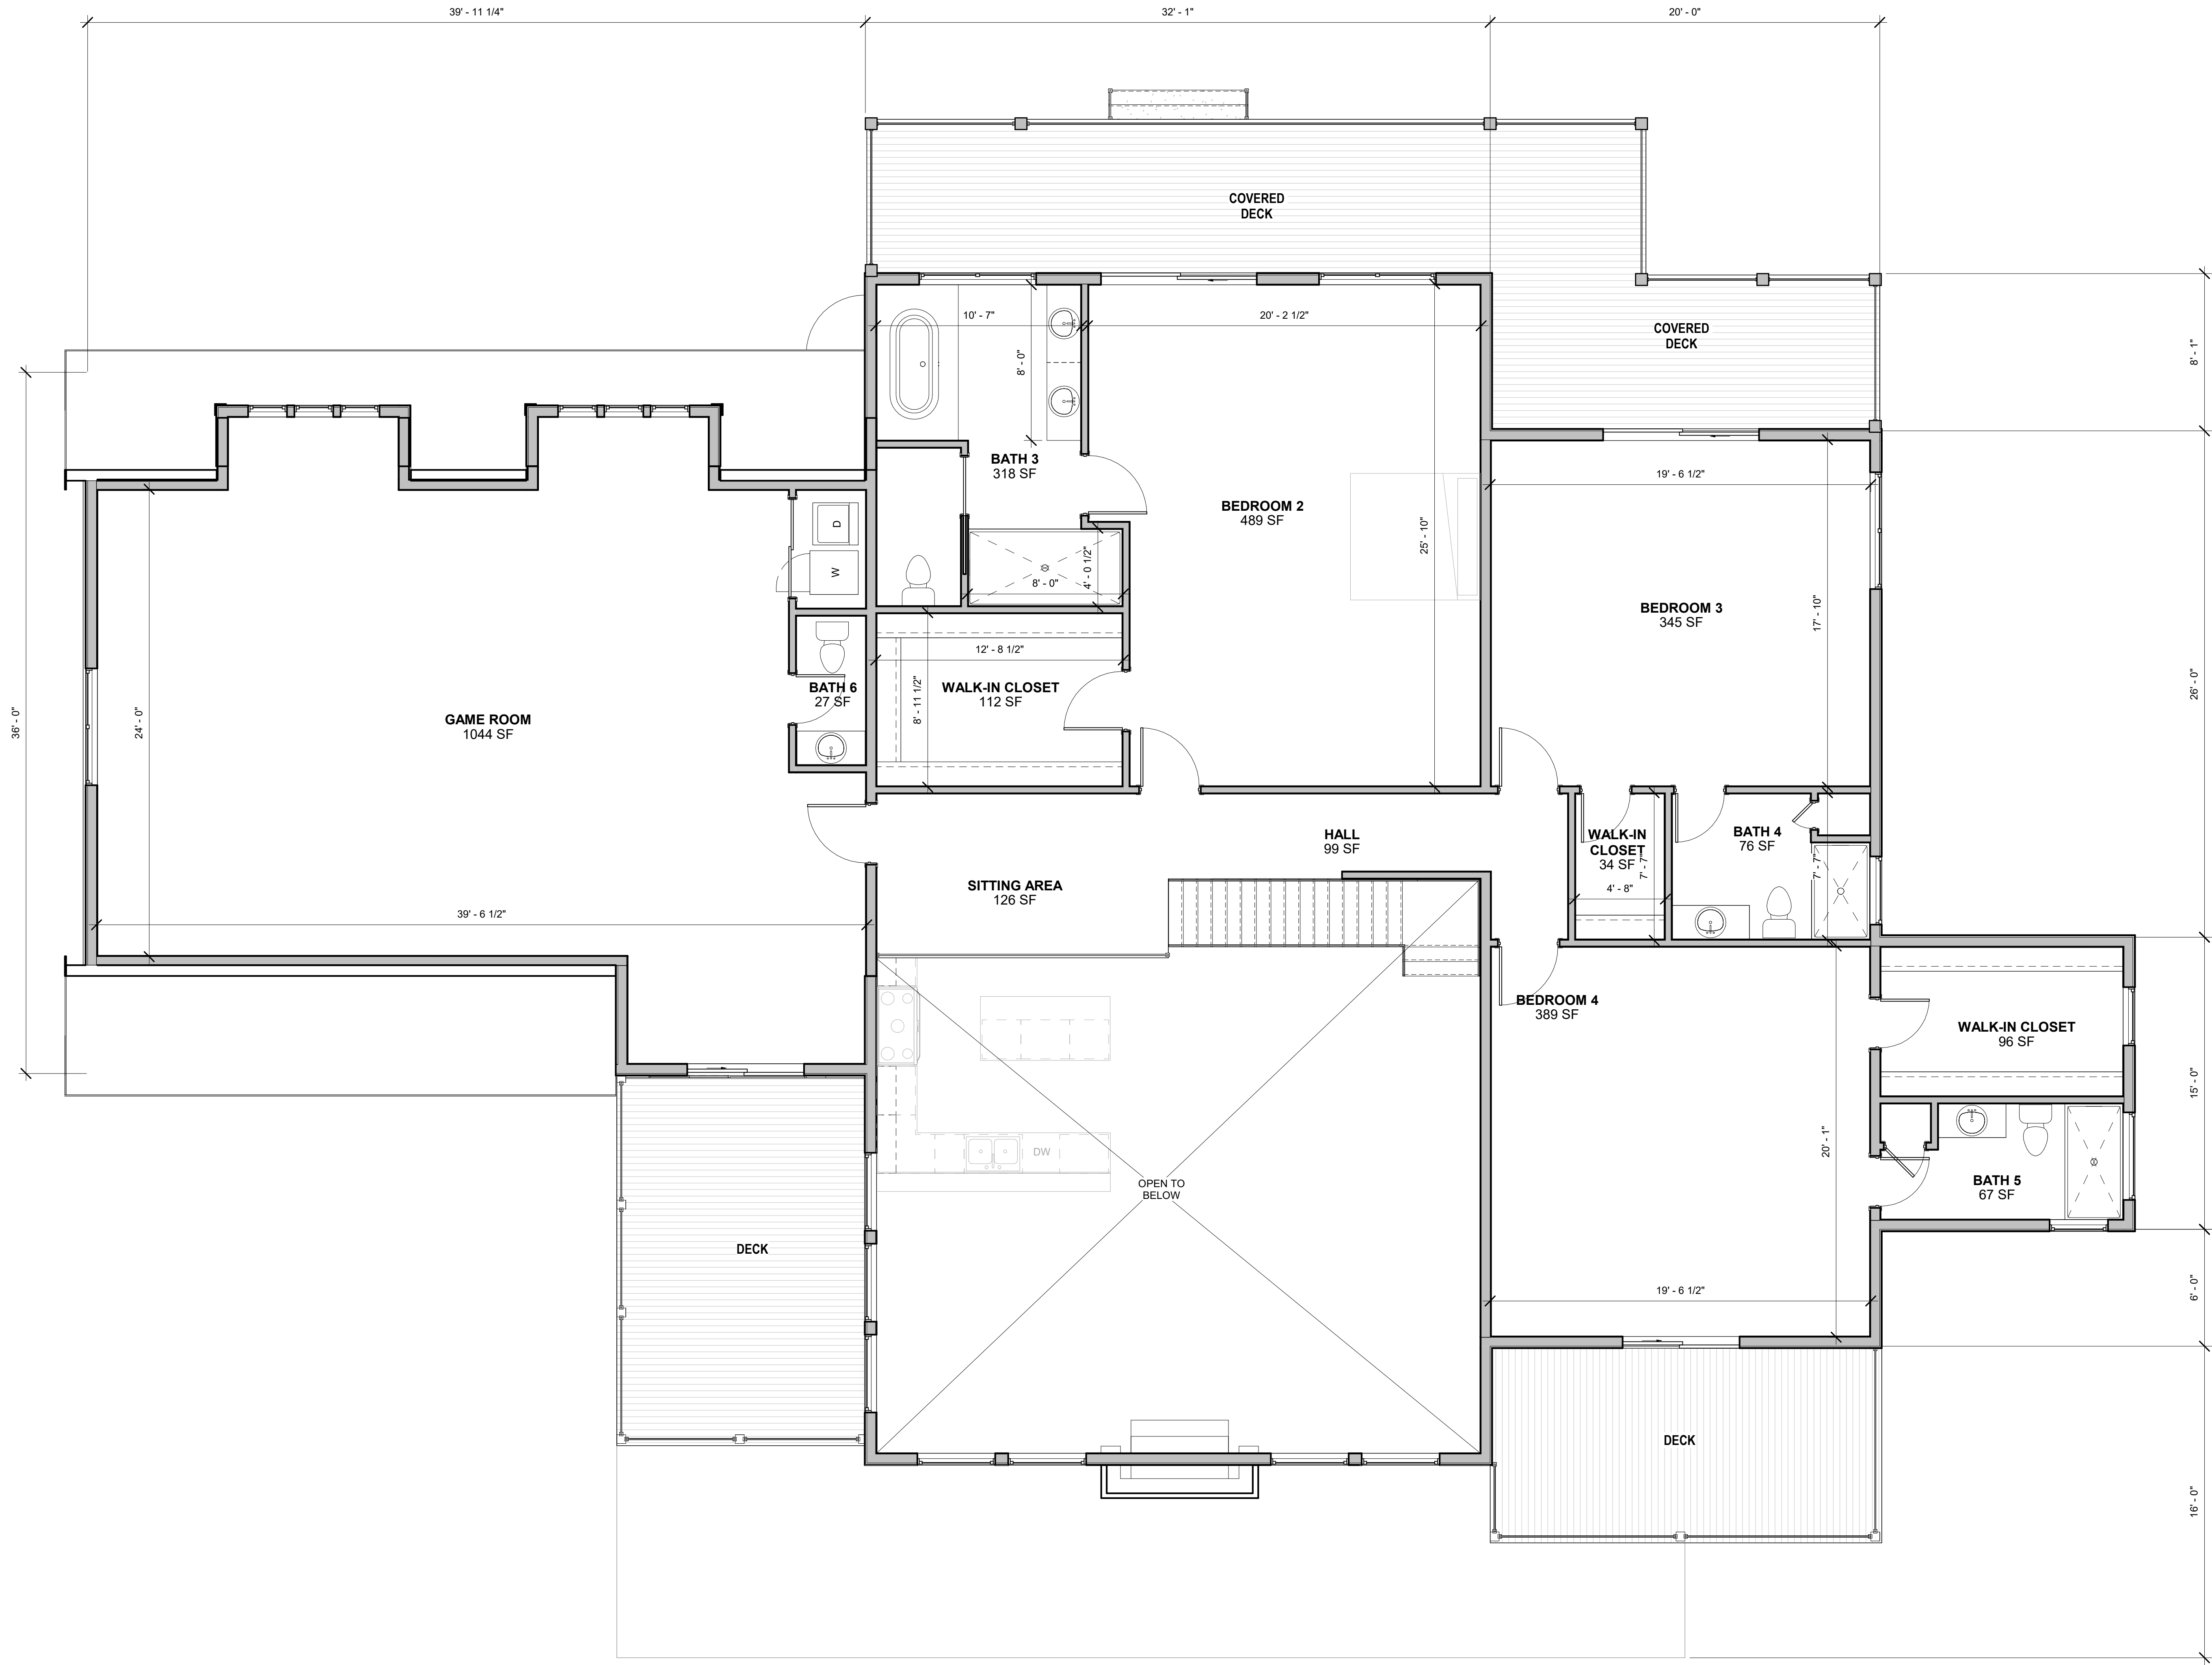

1 PROPOSED SECOND FLOOR

Ref: A201 / Scale: 1/4" = 1'-0"

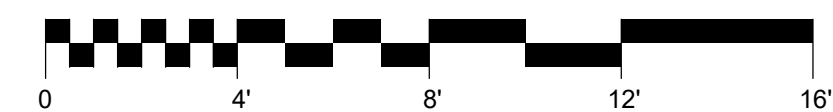

Project Location:

117 RED FOX RUN,
VESTAL, NY 13850

Project Name:

NEW RESIDENCE - ANELLO

Drawing Name:

PROPOSED SECOND
FLOOR PLAN

Designed by:

GRIFFITHS ENGINEERING

Drawn by:

DS

Checked by:

DS

Unauthorized alteration of
this drawing is a violation of
Professional Engineering Law, Section 2209,
sub-section 2.

Date:


07.31.2026

Project No.:

2026-106

Plot scale:

AS NOTED

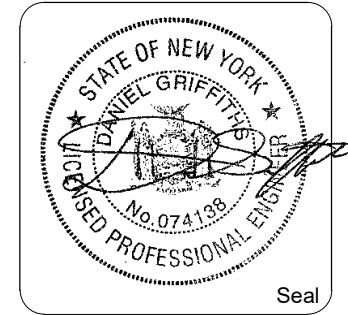

GRIFFITHS ENGINEERING
AND ARCHITECTURE, PLLC

33 Washington Street, Suite 2
Binghamton, New York 13903
T: (607) 724-2400
F: (607) 724-2436




Sheet Number:

A102




4 PROPOSED WEST ELEVATION
Ref: A101 / Scale: 1/8" = 1'-0"

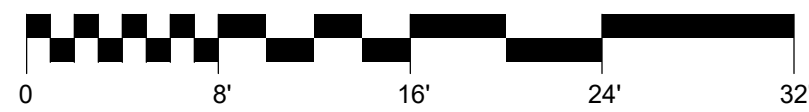

3 PROPOSED SOUTH ELEVATION
Ref: A101 / Scale: 1/8" = 1'-0"



2 PROPOSED EAST ELEVATION
Ref: A101 / Scale: 1/8" = 1'-0"

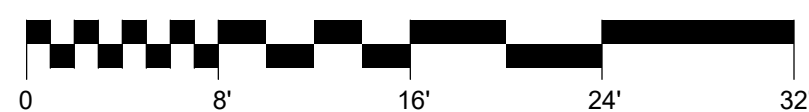

1 PROPOSED NORTH ELEVATION
Ref: A101 / Scale: 1/8" = 1'-0"

